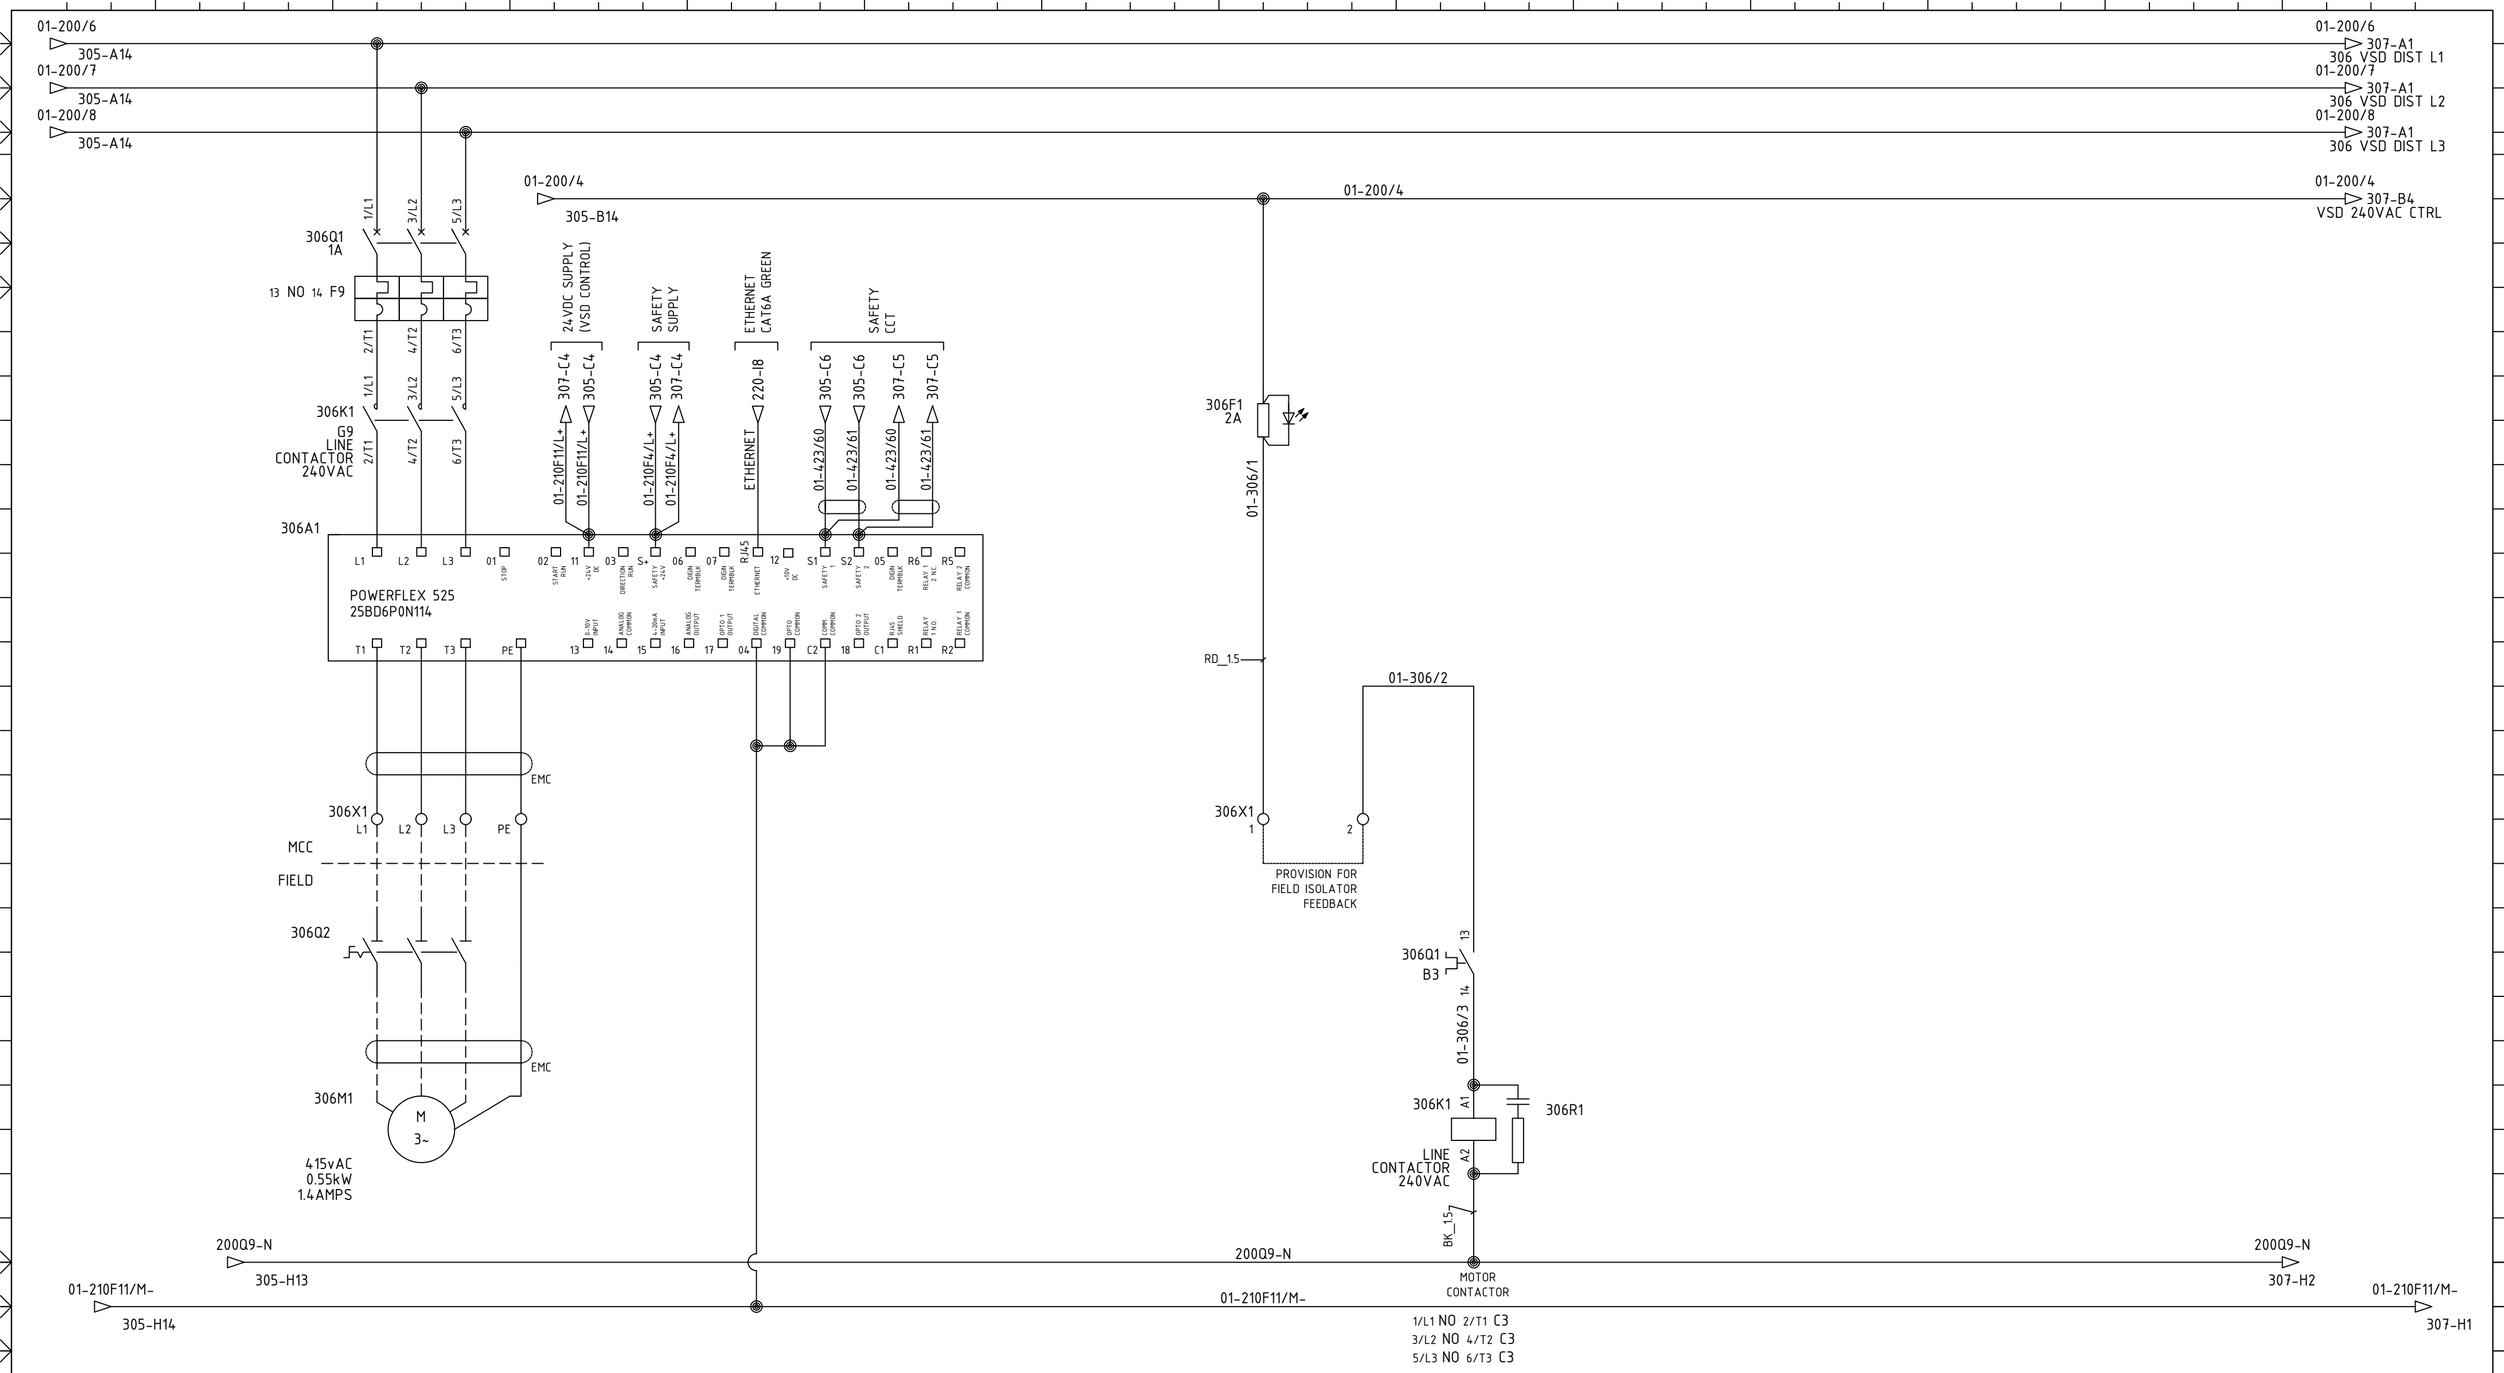

REV	DATE	DESCRIPTION
A	25/05/2022	FOR REVIEW

DOWNEY ENGINEERING
CONTROL SYSTEM INTEGRATION

1 / 532 ALDERLEY STREET
TOOWOOMBA QLD 4350
P: (07) 4613 6242
F: (07) 4613 6191
WEB: WWW.DOWNEYENG.COM.AU

© THIS WORK CANNOT BE REPRODUCED OR COPIED IN ANY FORM WITHOUT THE EXPRESS WRITTEN PERMISSION OF DOWNEY ENGINEERING.

CLIENT: MORT AND CO - GRASSDALE FEEDLOT

PROJECT: DE-OILING PLANT 1

TITLE: GR_C01_SB03_MV01
MICRO BATCH FEEDER
ELECTRICAL SCHEMATIC DIAGRAM

INSTALLATION: =C01

TOTAL SHEETS IN SET: 089

LOCATION: +MCC01

PREV: 305

SHEET: 306

SCALE: NTS (SYM @ A2)

NEXT: 307

PLOT DATE :2022-05-25

DOCUMENT: GR_C01_MCC01_306

DES: RLL	DRN: RLL	CHK:	APP:
DATE: 25/05/2022	DATE: 25/05/2022	DATE:	DATE:

FILE: P:\Client Data\Projects\22891 - Grassdale DeOiling Plant\Dwg\E\22891_E01_300.dwg